MUSLIM EDUCATIONAL CITY
AZAKHEL BELA

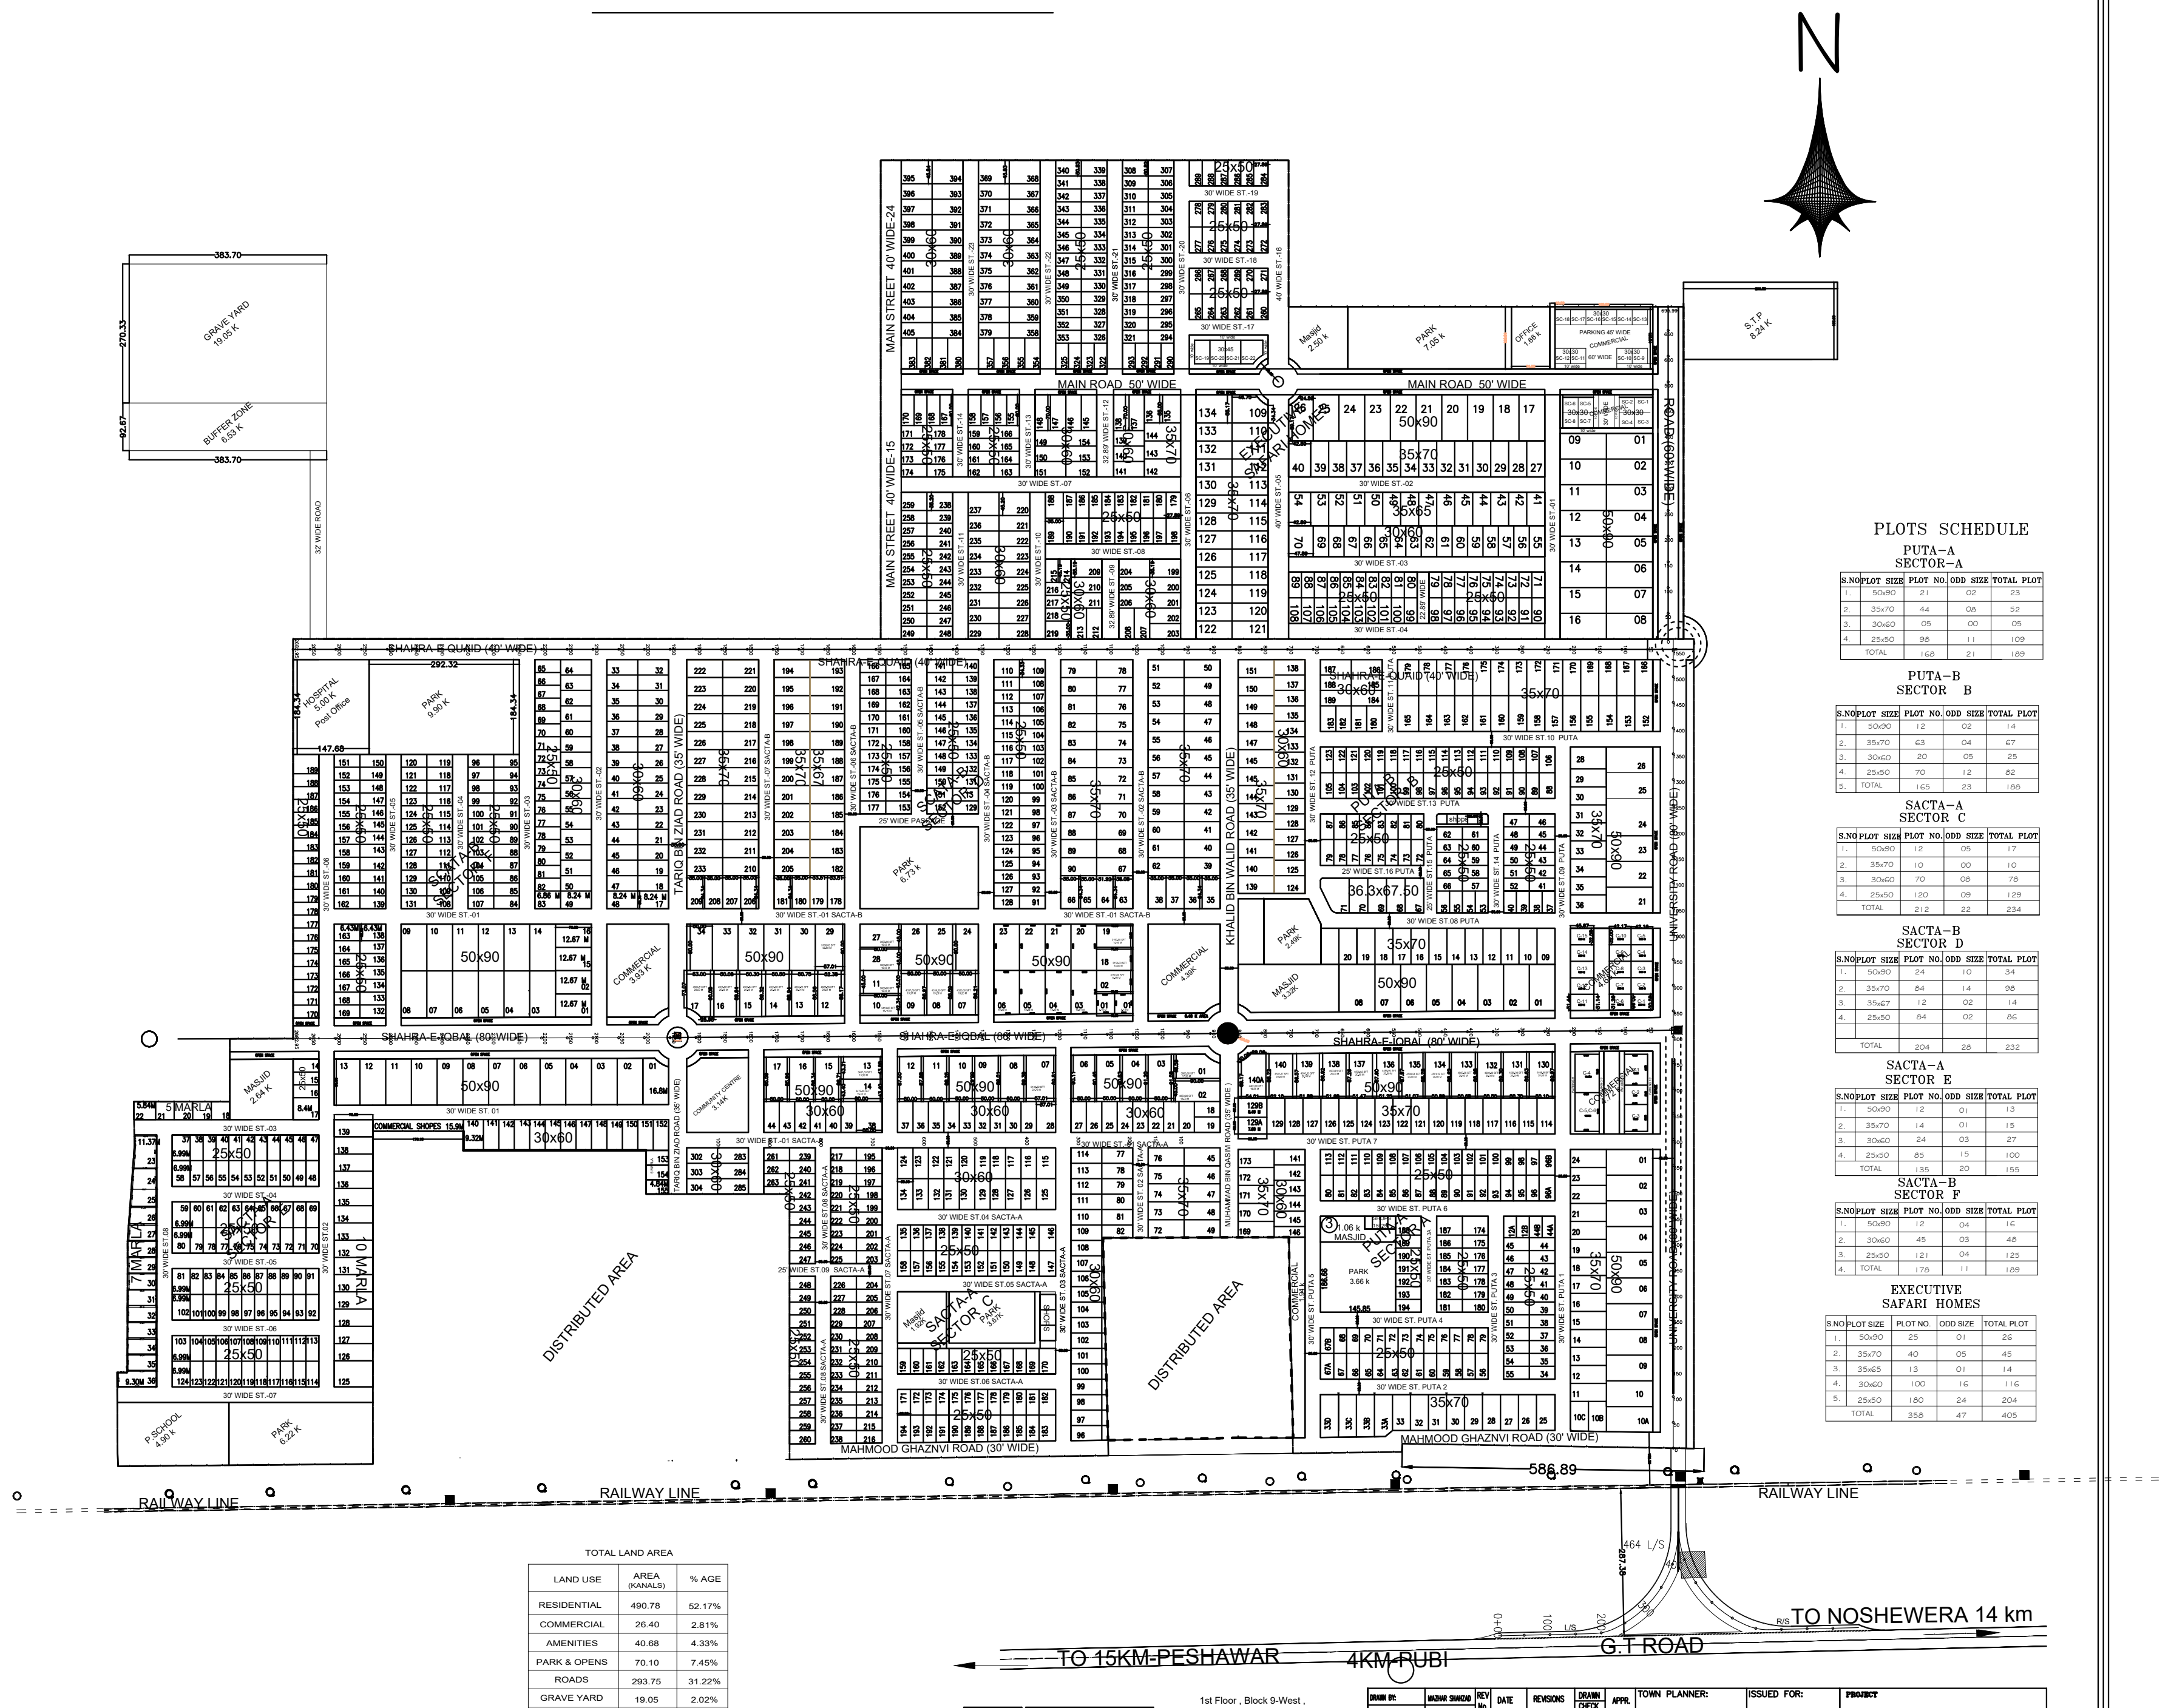

PLOTS SCHEDULE

PUTA–A
SECTOR–A

S.NO	PLOT SIZE	PLOT NO.	ODD SIZE	TOTAL PLOT
1.	50x90	21	02	23
2.	35x70	44	08	52
3.	30x60	05	00	05
4.	25x50	98	11	109
TOTAL		168	21	189

PUTA–B
SECTOR B

S.NO	PLOT SIZE	PLOT NO.	ODD SIZE	TOTAL PLOT
1.	50x90	12	02	14
2.	35x70	63	04	67
3.	30x60	20	05	25
4.	25x50	70	12	82
5.	TOTAL	165	23	188

SACTA–A
SECTOR C

S.NO	PLOT SIZE	PLOT NO.	ODD SIZE	TOTAL PLOT
1.	50x90	12	05	17
2.	35x70	10	00	10
3.	30x60	70	08	78
4.	25x50	120	09	129
TOTAL		212	22	234

SACTA–B
SECTOR D

S.NO	PLOT SIZE	PLOT NO.	ODD SIZE	TOTAL PLOT
1.	50x90	24	10	34
2.	35x70	84	14	98
3.	35x67	12	02	14
4.	25x50	84	02	86
TOTAL		204	28	232

SACTA–A
SECTOR E

S.NO	PLOT SIZE	PLOT NO.	ODD SIZE	TOTAL PLOT
1.	50x90	12	01	13
2.	35x70	14	01	15
3.	30x60	24	03	27
4.	25x50	85	15	100
TOTAL		135	20	155

SACTA–B
SECTOR F

S.NO	PLOT SIZE	PLOT NO.	ODD SIZE	TOTAL PLOT
1.	50x90	12	04	16
2.	30x60	45	03	48
3.	25x50	121	04	125
4.	TOTAL	178	11	189

EXECUTIVE
SAFARI HOMES

S.NO	PLOT SIZE	PLOT NO.	ODD SIZE	TOTAL PLOT
1.	50x90	25	01	26
2.	35x70	40	05	45
3.	35x65	13	01	14
4.	30x60	100	16	116
5.	25x50	180	24	204
TOTAL		358	47	405

TOTAL LAND AREA

LAND USE	AREA (KANALS)	% AGE
RESIDENTIAL	490.78	52.17%
COMMERCIAL	26.40	2.81%
AMENITIES	40.68	4.33%
PARK & OPENS	70.10	7.45%
ROADS	293.75	31.22%
GRAVE YARD	19.05	2.02%
TOTAL	940.76	100

TOTAL =940.75 kanal

Designmen
CONSULTING ENGINEERS (Pvt) LTD.

1st Floor , Block 9-West ,
Rizwan Plaza. Jinnah Avenue
F-6 , ISLAMABAD - PAKISTAN
Ph: 92-51-2828577 , 2829002
Fax : 92-51-2829891
E-mail: najib@isb.comsats.net.pk

		REV No.	DATE	REVISIONS	DRAWN CHECK	APPR.
DRAWN BY:	MAZHAR SHAHZAD					
DESIGN BY:	AZHAR ALI					
QAG CHECK:	MAZHAR SHAHZAD					
CAD CHECK:	MAZHAR SHAHZAD					
APPROVED BY:	MUJIB AHMED					

TOWN PLANNER:

CLIENT: MUSLIM ENTERPRISES

ISSUED FOR: APPROVAL/NOC

TYPE OF DRAWING

PROJECT: MUSLIM EDUCATIONAL CITY AZAKHAIL NOWSHERA

TITLE: TOPO GRAPHIC SURVEY

SCALE: 1=1000

DATE:

DRAWING NUMBER: 01

REVISION: 01